


Schnitt A-A Treppe T1 und Galeriebühne M 1:50

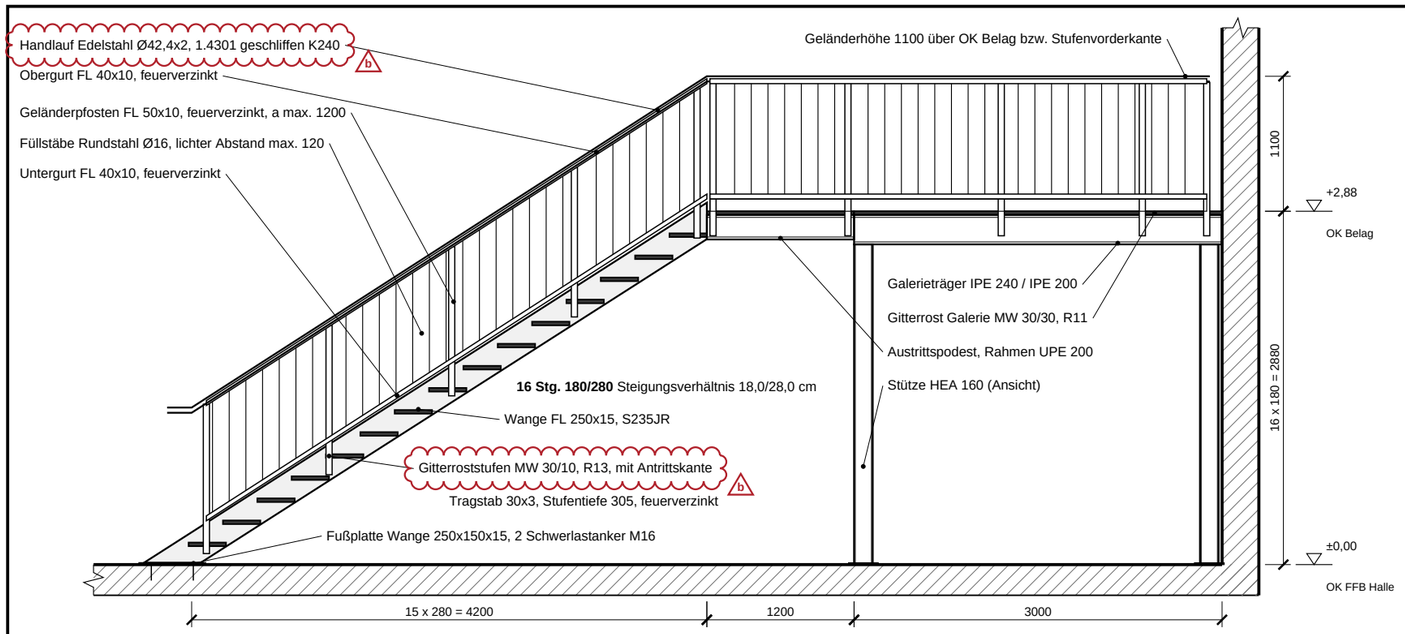

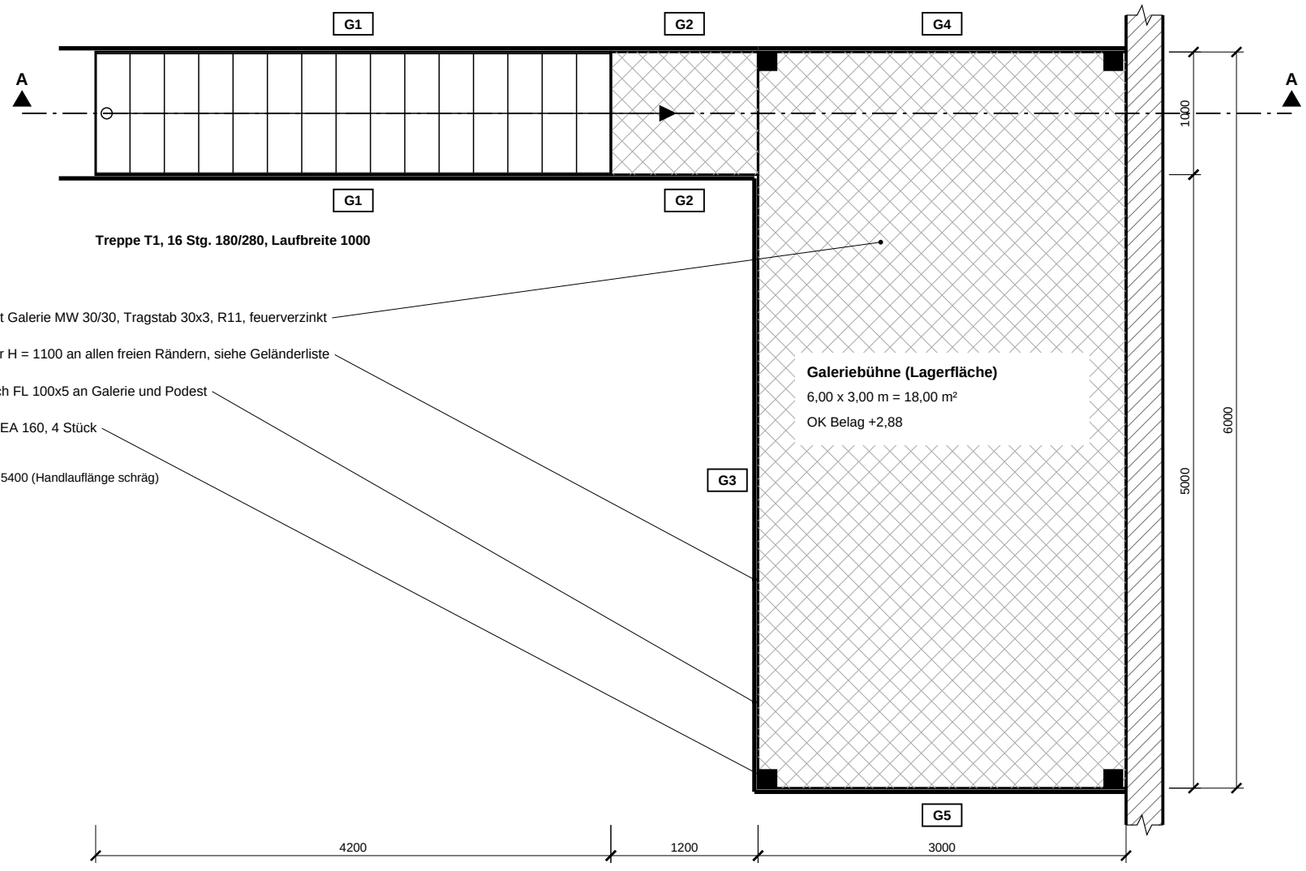


Draufsicht Galeriebühne mit Treppe T1 M 1:50

Detail 1 Pfostenanschluss an Wange M 1:10

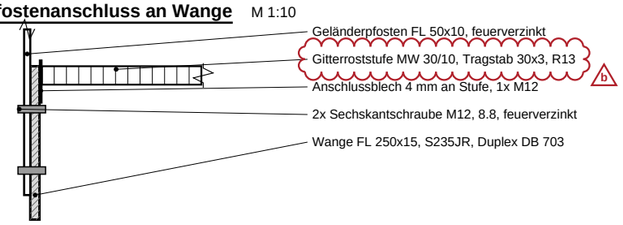

Detail 2 Wandhandlauf Treppenhaus Sozialtrakt M 1:5

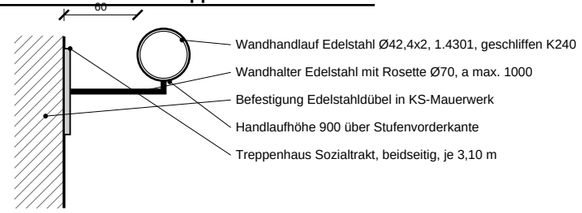

Geländerliste Treppe T1 und Galeriebühne

Pos.	Bauteil	Länge
G1	Treppengeländer Treppe T1, beidseitig, je 5,40 m	10,80 m
G2	Podestgeländer Austrittspodest, beidseitig, je 1,20 m	2,40 m
G3	Galeriegeländer Längsseite	5,00 m
G4	Galeriegeländer Stirnseite an Treppe	3,00 m
G5	Galeriegeländer Stirnseite gegenüber	3,00 m
	Summe Geländer H = 1100, Handlauf Edelstahl	**24,20 m**
	Bordblech FL 100x5 an Galerie und Podest	13,40 m
	Wandhandlauf Treppenhaus Sozialtrakt (Detail 2)	6,20 m

Allgemeine Hinweise

1. Alle Maße in mm, Höhen in m bezogen auf OK FFB Halle ±0,00. Maße vor Fertigung am Bau prüfen.
2. Stahl S235JR, Ausführungsklasse EXC2 nach DIN EN 1090-2.
3. Korrosionsschutz Stahlteile: feuerverzinkt + Duplex-Beschichtung DB 703.
4. Gitterroste und Gitterroststufen feuerverzinkt, ohne Beschichtung.
5. Edelstahlteile 1.4301, geschliffen K240, Verbindungsmittel A4.
6. Holmlast 1,0 kN/m, lichte Öffnungen max. 120 mm.
7. Statik und Werkstattplanung durch den AN, siehe LV.

Änderungen

Index	Datum	Änderung	gez.
a	18.09.2026	Galeriegeländer G5 ergänzt	BA
b	12.10.2026	Handlauf Edelstahl, Gitterroststufen MW 30/10, R13 (Nutzerabstimmung)	BA

Bauherr
Gemeinde Musterstadt, Der Bürgermeister, Rathausplatz 1, 12345 Musterstadt

Bauvorhaben
Neubau Feuerwehrgerätehaus Musterstadt, Am Gerätehaus 3, 12345 Musterstadt

Planinhalt
Treppe T1 und Geländer Galeriebühne
Schnitt A-A, Draufsicht, Details 1 und 2

Planart
Ausführungsplanung, Anlage zum LV Los 12 Stahlbau- und Schlosserarbeiten, Vergabe-Nr. MS-2026-12

Plan-Nr.	Index	Maßstab	Format	Datum	gez. / gepr.	Status
TW-01	**b**	1:50 / 1:10 / 1:5	A3	12.10.2026	BA / MB	Ausschreibung

Planverfasser
Planungsbüro Beispiel Architekten
Musterstraße 5, 12345 Musterstadt

Unterschrift Planverfasser