

Ansicht Achse A M 1:50

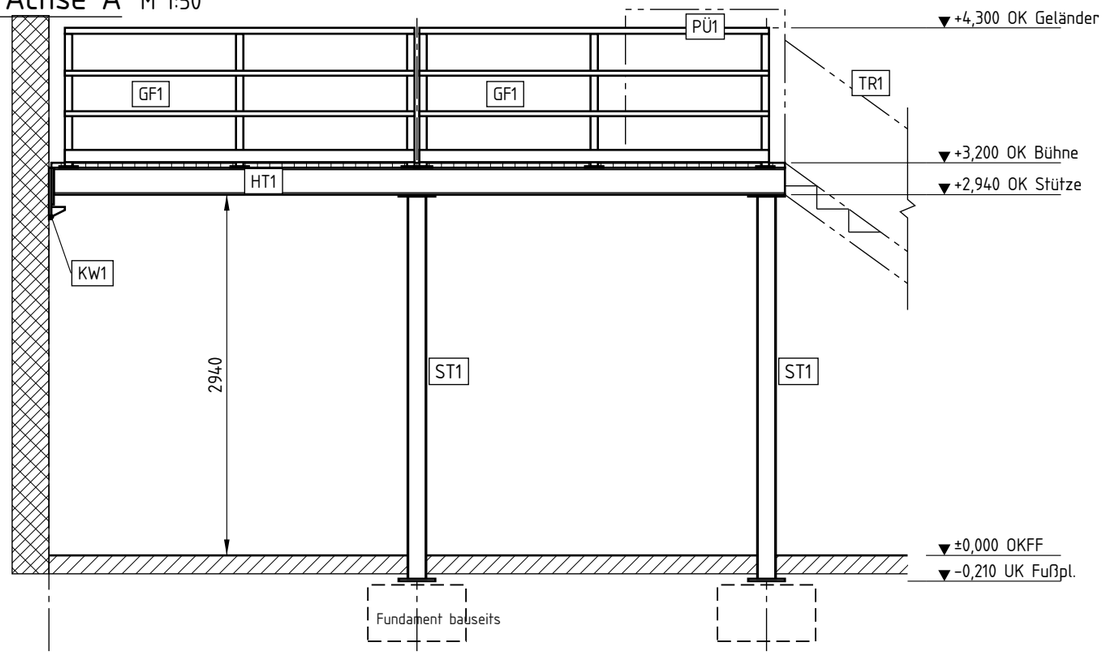

Draufsicht M 1:50

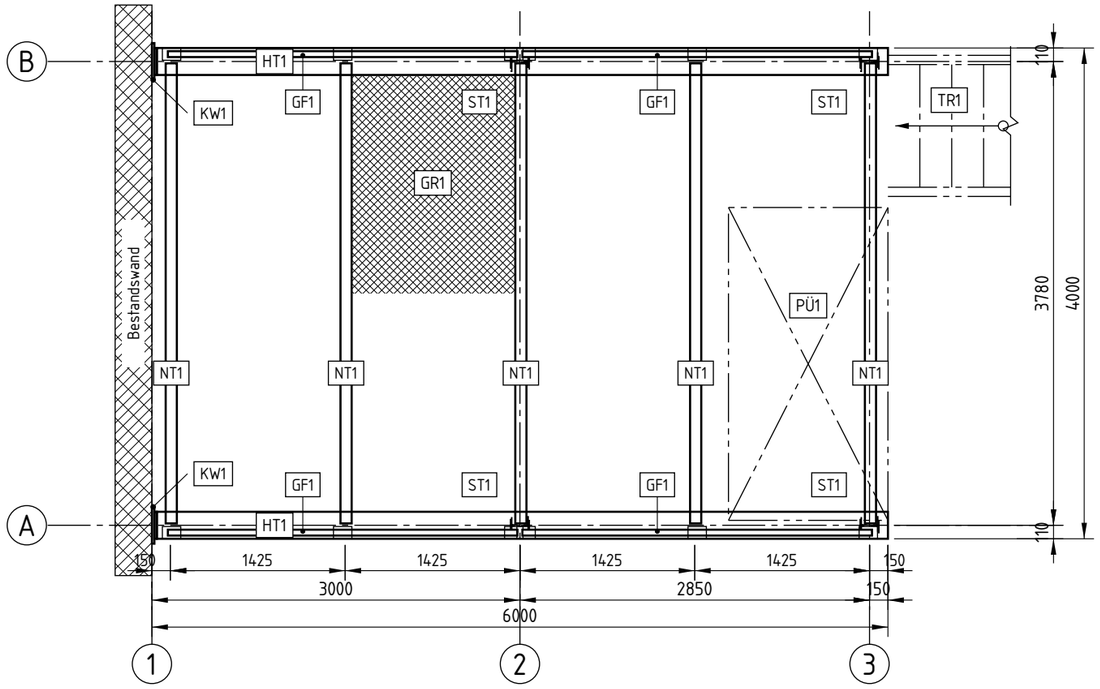

Positionsliste Baugruppen

Marke	Menge	Einh.	Benennung	Zeichnung / Norm	Einzelgew. kg	Gesamtgew. kg
ST1	4	Stk	Stütze HEA 160, L = 3150	BM-26-115-110	118,24	472,96
HT1	2	Stk	Hauptträger HEB 220 (1x spiegelbildl.)	BM-26-115-120	453,94	907,88
NT1	5	Stk	Nebenträger IPE 180, L = 3750	BM-26-115-130	70,50	352,50
GF1	4	Stk	Geländerfeld L = 2850	BM-26-115-140	54,36	217,44
KW1	2	Stk	Anschlusskonsole Wand	BM-26-115-150	18,40	36,80
GR1	23,92	m²	Gitterrost MW 30/30, TS 40x3, R11	Kaufteil, DIN 24537-1	38,60 /m²	923,31
	64	Stk	Gitterrost-Klemmhalter M8	Kaufteil	0,080	5,12
	16	Stk	HV-Garnitur M20x65-10.9 (HT1/ST1)	EN 14399-4, fvz	0,39	6,24
	12	Stk	HV-Garnitur M20x70-10.9 (HT1/KW1)	EN 14399-4, fvz	0,40	4,80
	20	Stk	Garnitur M16x45-8.8 (NT1/HT1)	ISO 4017/4032/7089	0,15	3,00
	48	Stk	Garnitur M12x40-8.8 (GF1/HT1)	ISO 4017/4032/7089	0,080	3,84
	16	Stk	Schwerlastanker M20 (ST1)	Kaufteil, nach ETA	0,63	10,08
TR1	1	Stk	Treppe 17 Stg., Laufbreite 1000	Kaufteil, Herstellerzeichn.	430,00	430,00
PÜ1	1	Stk	Paletten-Übergabestation 2500	Kaufteil, Herstellerzeichn.	240,00	240,00
			Summe Stahlbau Eigenfertigung			**1987,58**
			Gesamtgewicht inkl. Kaufteile			**3613,97**

Hinweise

1. Ausführung nach DIN EN 1090-2, EXC2. Statik: Nachweis S-26-115 vom 08.10.2026.
2. Nutzlast Lagerbühne 5,0 kN/m², Einzellast 3,0 kN. OK Bühne +3,200.
3. Werkstoff S235JR, Hohlprofile S235JRH. HV-Garnituren EN 14399-4, 10.9.
4. Korrosionsschutz Stahlbau: gestrahlt Sa 2½, GB EP 80 µm, DB PUR 80 µm RAL 7016. Gitterroste und Verbindungsmittel feuerverzinkt.
5. Stützen auf Einzelfundamente (bauseits), Untermörtelung 30 mm, Verankerung mit Schwerlastankern M20 nach ETA.
6. HT1 wandseitig über Anschlusskonsole KW1 an Bestandswand (STB).
7. Gitterrost an Pfostenfußplatten GF1 ausklinken, Befestigung mit Klemmhaltern.
8. TR1 und PÜ1 Kaufteile, Lieferung und Anschluss nach Herstellerzeichnung.
9. Alle Maße in mm. Maße am Bau prüfen.

Index	Änderung	Datum	Name
-	Erstausgabe, Freigabe zur Fertigung	19.10.2026	T. Rehm

Werkstoff: S235JR	Oberfläche / Korrosionsschutz: gestrahlt Sa 2½, GB EP 80 µm, DB RAL 7016		Gewicht: **3613,97 kg**
Allgemeintoleranzen: ISO 2768-mK	Schweißkonstruktionen: ISO 13920-BF	Ausführungsklasse: EXC2 (EN 1090-2)	Datum: 10/2026
Maßstab: 1:50	Format: A3	Projektion:	Auftrag: 26-115 / Blatt: **1 / 5**

	Datum	Name
Bearb.	15.10.2026	M. Kranz
Gepr.	19.10.2026	T. Rehm
Freig.	19.10.2026	T. Rehm

Projekt: Erweiterung Lagerhalle 2
Kunde: Musterbau Projekt GmbH
Bauteil / Position: Lagerbühne LB-01, Achsen 1-3 / A-B


Beispiel Metallbau GmbH
Stahl- und Metallbau
Industriestraße 12, 12345 Musterstadt
Schutzvermerk ISO 16016 beachten

Benennung: **Lagerbühne LB-01**
Übersicht / Zusammenbau, Positionsliste

Zeichnungsnummer: **BM-26-115-100**
Index: **-**


Ansicht A M 1:15

Blick auf Flansch

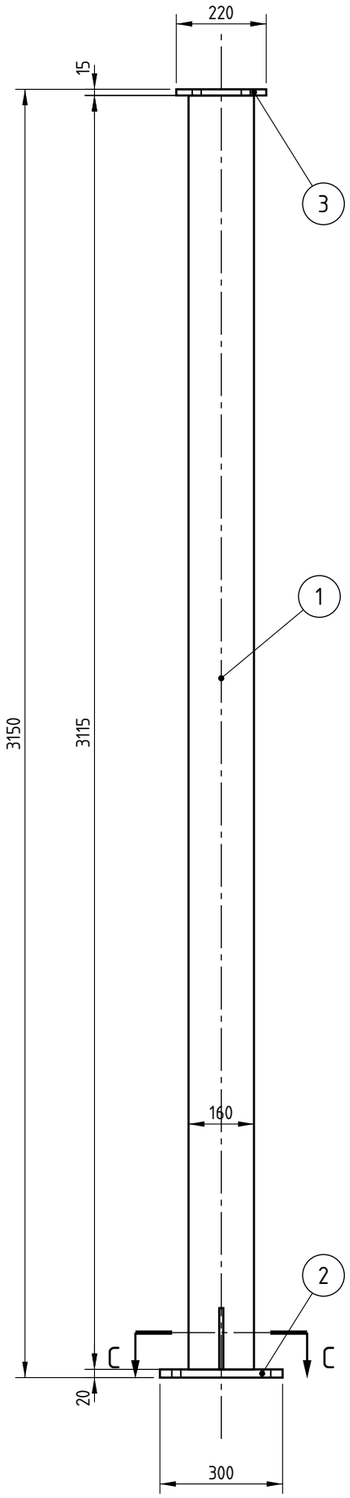


Ansicht B M 1:15

Blick auf Steg

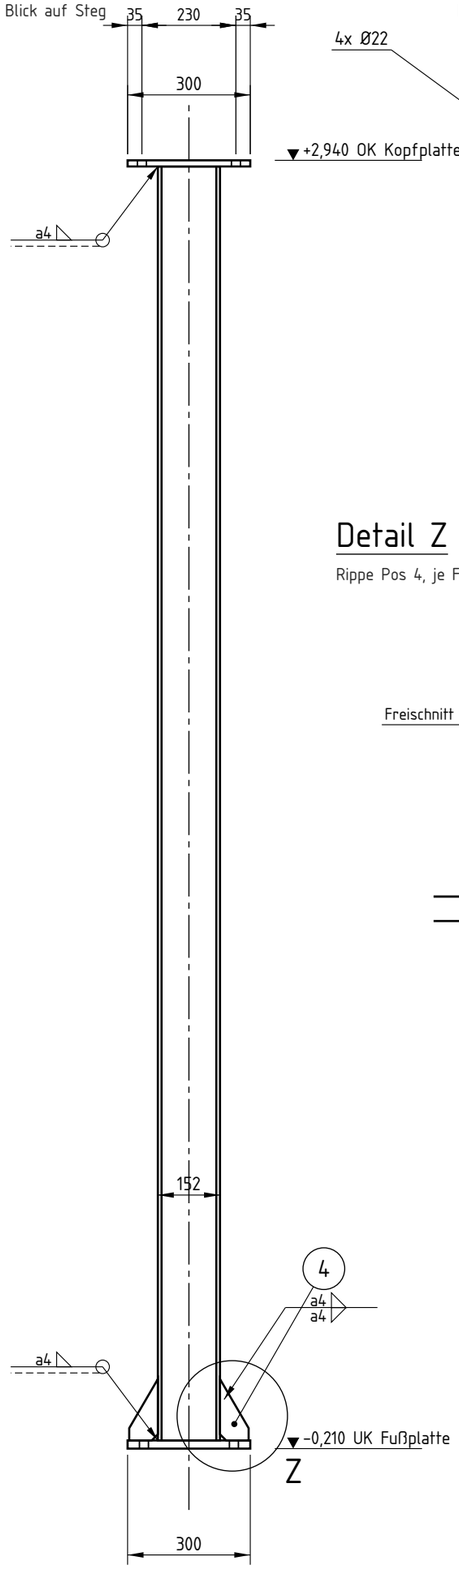


Draufsicht M 1:5

Kopfplatte Pos 3, BL 15

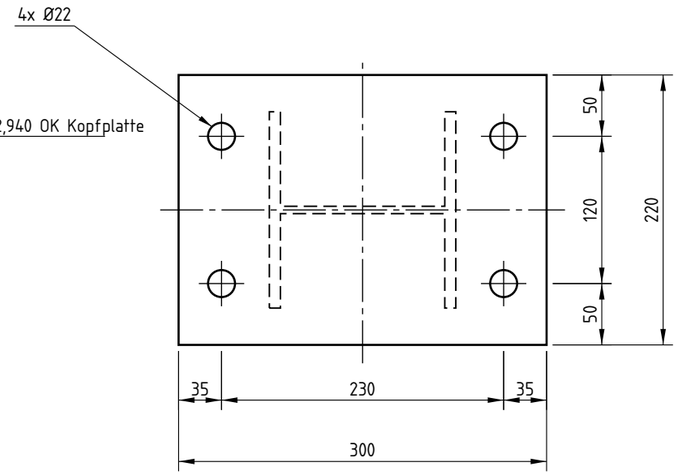


Schnitt C-C M 1:5

Fußplatte Pos 2, BL 20

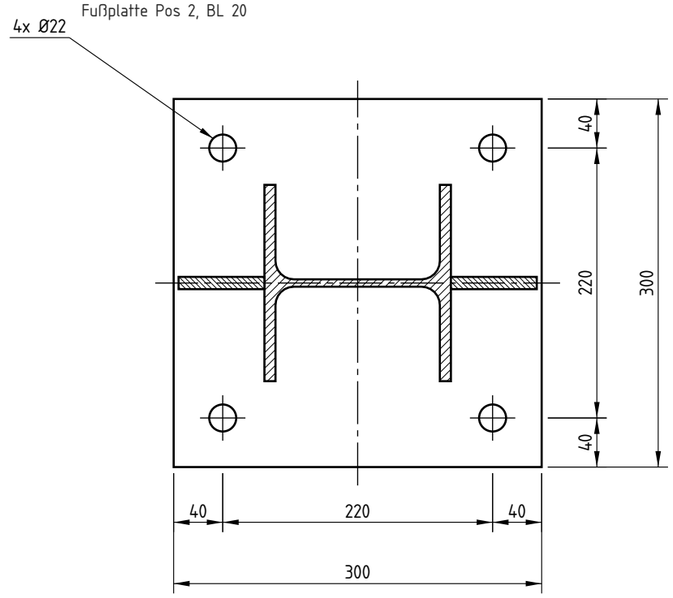

Detail Z M 1:5

Rippe Pos 4, je Flanschseite

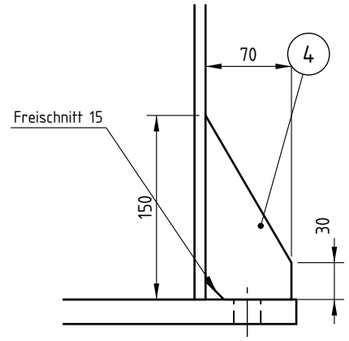

Hinweise

Anzahl: 4 Stück (Achsen A-2, A-3, B-2, B-3).
Schweißnähte a4 umlaufend, soweit nicht anders angegeben.
Fußplatte vollflächig untermörteln (30 mm), Anker M20 nach ETA.
Kopfplatte: Anschluss HT1 mit 4x HV M20x65-10.9.
Korrosionsschutz siehe Schriftfeld, Kontaktflächen HV frei.

Stückliste ST1 (je Stück)

Pos	Stk	Benennung	Halbzeug	Werkstoff	Länge mm	Einzelgew. kg	Gesamtgew. kg
1	1	Stütze	HEA 160	S235JR	3115	94,70	94,70
2	1	Fußplatte	BL 20x300	S235JR	300	14,13	14,13
3	1	Kopfplatte	BL 15x220	S235JR	300	7,77	7,77
4	2	Rippe	BL 10x70	S235JR	150	0,82	1,64
		Gewicht je Baugruppe					**118,24**
		Gesamt 4 Stk					**472,96**

-	Erstausgabe, Freigabe zur Fertigung	19.10.2026	T. Rehm
Index	Änderung	Datum	Name

Werkstoff: S235JR	Oberfläche / Korrosionsschutz: gestrahlt Sa 2½, GB EP 80 µm, DB RAL 7016		Gewicht: **118,24 kg/Stk**
Allgemeintoleranzen: ISO 2768-mK	Schweißkonstruktionen: ISO 13920-BF	Ausführungsklasse: EXC2 (EN 1090-2)	Datum: 10/2026
Maßstab: 1:15 / 1:5	Format: A3 — Projektion: ⇥	Auftrag: 26-115	Blatt: **2 / 5**

	Datum	Name
Bearb.	15.10.2026	M. Kranz
Gepr.	19.10.2026	T. Rehm
Freig.	19.10.2026	T. Rehm

Projekt: Erweiterung Lagerhalle 2
Kunde: Musterbau Projekt GmbH
Bauteil / Position: ST1, Achsen A/B-2/3

Beispiel Metallbau GmbH
Stahl- und Metallbau
Industriestraße 12, 12345 Musterstadt


Schutzvermerk ISO 16016 beachten

Benennung: **Stütze ST1**
Zusammenbau HEA 160, L = 3150, 4 Stück

Zeichnungsnummer: **BM-26-115-110**


Index: **-**

Untersicht M 1:20

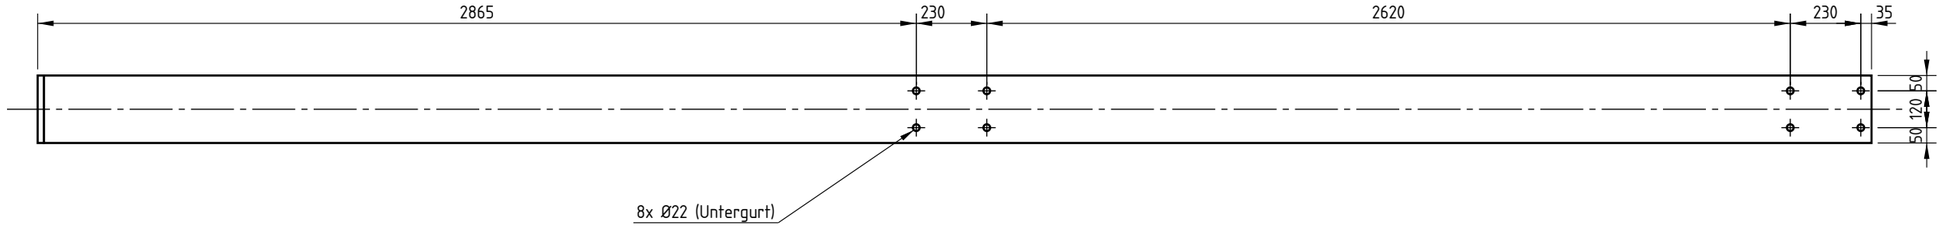


Ansicht M 1:20

von Innenseite (Seite NT1)

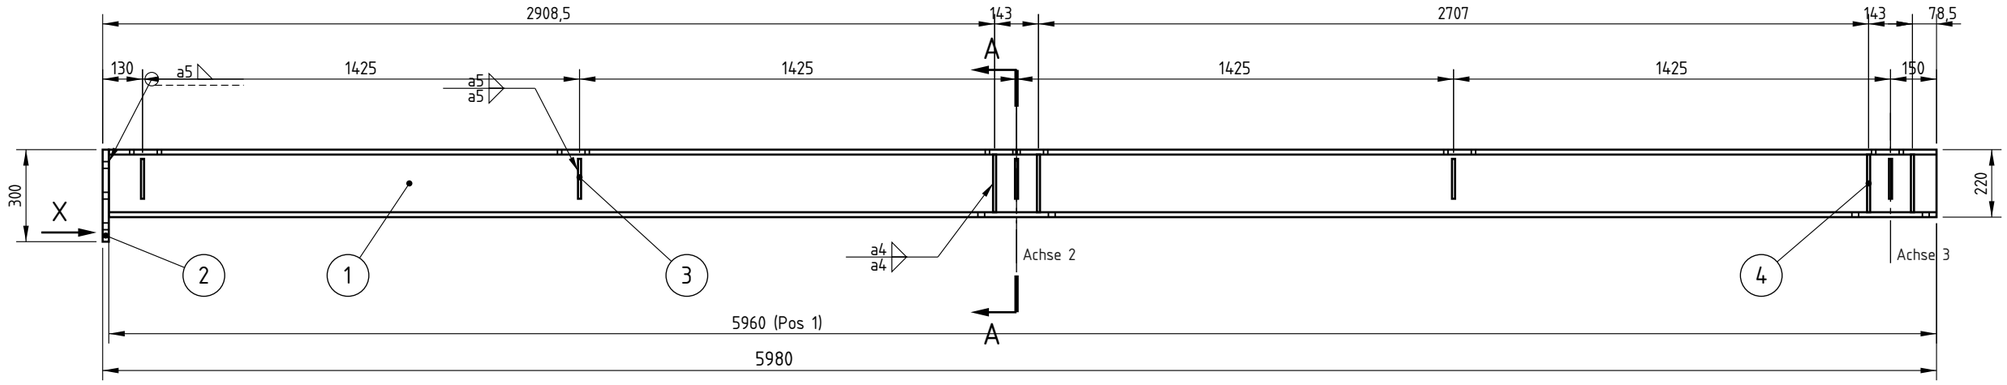


Draufsicht M 1:20

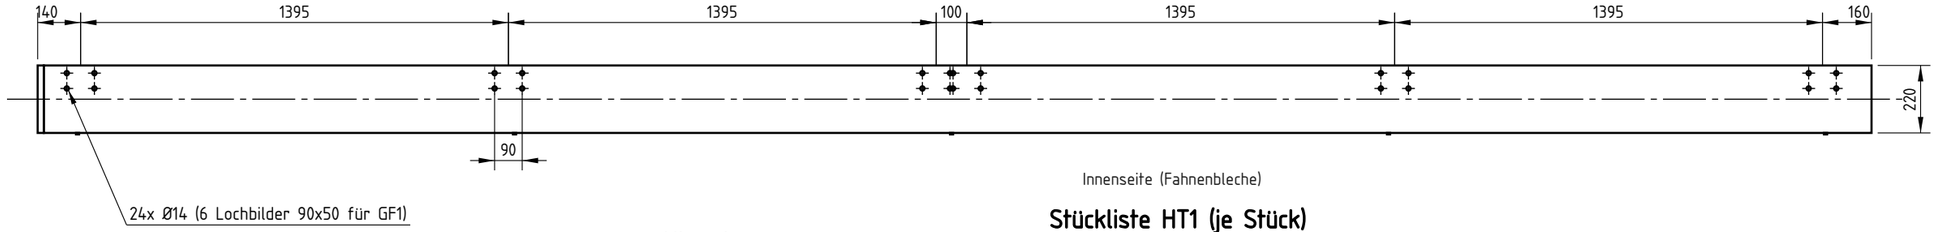

Innenseite (Fahnenbleche)


Schnitt A-A M 1:10

Auflager Achse 2 (Achse 3 gleich)

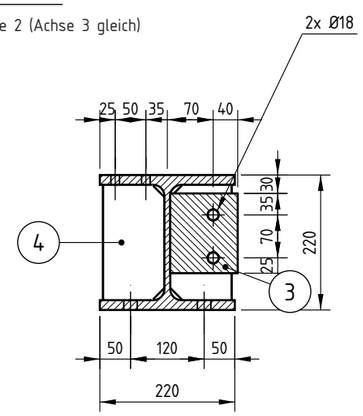

Ansicht X M 1:10

Stirnplatte Pos 2, BL 20

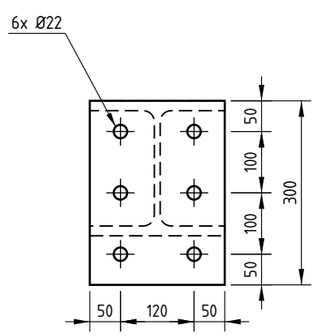

Hinweise

2 Stück: 1x wie gezeichnet (Achse A),
1x spiegelbildlich (Achse B).
Schweißnähte a4, soweit nicht angegeben.
Kontaktflächen Stirnplatte und Untergurt
am Auflager HV-gerecht, ohne Deckbeschichtung.

Stückliste HT1 (je Stück)

Pos	Stk	Benennung	Halbzeug	Werkstoff	Länge mm	Einzelgew. kg	Gesamtgew. kg
1	1	Hauptträger	HEB 220	S235JR	5960	426,14	426,14
2	1	Stirnplatte	BL 20x220	S235JR	300	10,36	10,36
3	5	Fahnenblech	BL 10x110	S235JR	130	1,12	5,60
4	8	Steife	BL 10x100	S235JR	188	1,48	11,84
		Gewicht je Baugruppe					**453,94**
		Gesamt 2 Stk					**907,88**

Index	Änderung	Datum	Name
a	Bohrungen Geländer GF1 im Obergurt ergänzt	22.10.2026	M. Kranz
–	Erstausgabe, Freigabe zur Fertigung	19.10.2026	T. Rehm

Werkstoff: S235JR	Oberfläche / Korrosionsschutz: gestrahlt Sa 2½, GB EP 80 µm, DB RAL 7016		Gewicht: **453,94 kg/Stk**
Allgemeintoleranzen: ISO 2768-mK	Schweißkonstruktionen: ISO 13920-BF	Ausführungsklasse: EXC2 (EN 1090-2)	Datum: 10/2026
Maßstab: 1:20 / 1:10	Format: A3	Projektion	Auftrag: 26-115 / Blatt: 3 / 5

	Datum	Name
Bearb.	15.10.2026	M. Kranz
Gepr.	19.10.2026	T. Rehm
Freig.	19.10.2026	T. Rehm

Projekt: Erweiterung Lagerhalle 2
Kunde: Musterbau Projekt GmbH
Bauteil / Position: HT1, Achse A und B

Beispiel Metallbau GmbH
Stahl- und Metallbau
Industriestraße 12, 12345 Musterstadt

Schutzvermerk ISO 16016 beachten


Benennung: **Hauptträger HT1**
Zusammenbau HEB 220, L = 5980, 2 Stück

Zeichnungsnummer: **BM-26-115-120**


Index: **a**

Ansicht M 1:10

Steg liegt an Fahnenblech HT1

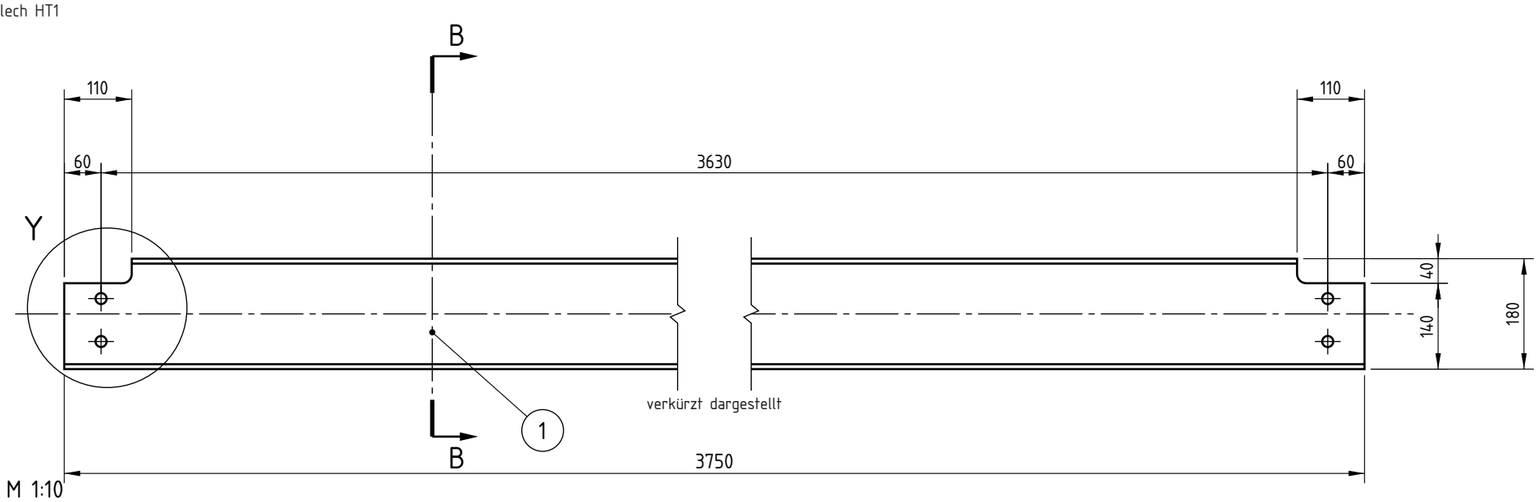

Draufsicht M 1:10

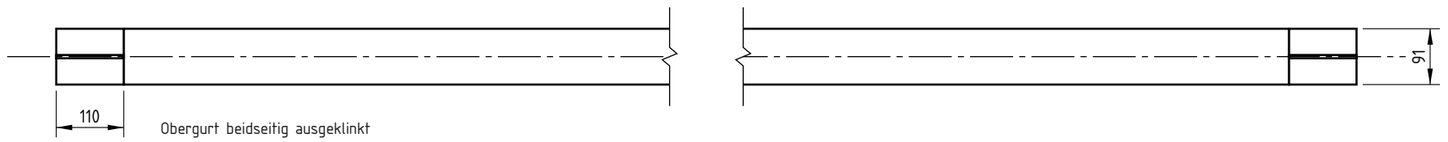


Hinweise

Anzahl: 5 Stück, alle gleich.
Ausklinkungen gesägt oder gebrannt,
Radius R15 kerbfrei verschliffen.
Anschluss an HT1 mit je 2x M16x45-8.8 (Ø18).


Detail Y M 1:5

Trägerende, beidseitig gleich

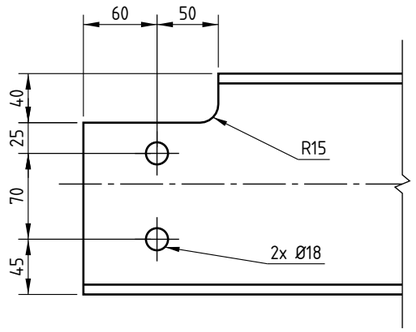

Schnitt B-B M 1:5

IPE 180, S235JR

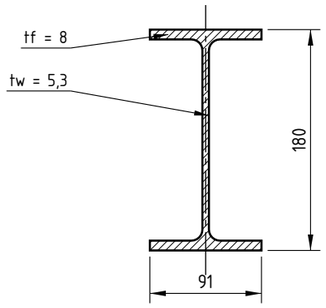

Stückliste NT1 (je Stück)

Pos	Stk	Benennung	Halbzeug	Werkstoff	Länge mm	Einzelgew. kg	Gesamtgew. kg
1	1	Nebenträger	IPE 180	S235JR	3750	70,50	70,50
		Gewicht je Baugruppe					**70,50**
		Gesamt 5 Stk					**352,50**

-	Erstausgabe, Freigabe zur Fertigung	19.10.2026	T. Rehm
Index	Änderung	Datum	Name

Werkstoff: S235JR	Oberfläche / Korrosionsschutz: gestrahlt Sa 2½, GB EP 80 µm, DB RAL 7016		Gewicht: **70,50 kg/Stk**
Allgemeintoleranzen: ISO 2768-mK	Schweißkonstruktionen: ISO 13920-BF	Ausführungsklasse: EXC2 (EN 1090-2)	Datum: 10/2026
Maßstab: 1:10 / 1:5	Format: A3 — Projektion	Auftrag: 26-115	Blatt: **4 / 5**

	Datum	Name
Bearb.	15.10.2026	M. Kranz
Gepr.	19.10.2026	T. Rehm
Freig.	19.10.2026	T. Rehm

Projekt: Erweiterung Lagerhalle 2
Kunde: Musterbau Projekt GmbH
Bauteil / Position: NT1, zwischen HT1 Achse A/B

Beispiel Metallbau GmbH
Stahl- und Metallbau
Industriestraße 12, 12345 Musterstadt

Schutzvermerk ISO 16016 beachten


Benennung: **Nebenträger NT1**
Einzelteil IPE 180, L = 3750, 5 Stück

Zeichnungsnummer: **BM-26-115-130**


Index: **-**

Ansicht M 1:15

von Bühnenseite (innen)

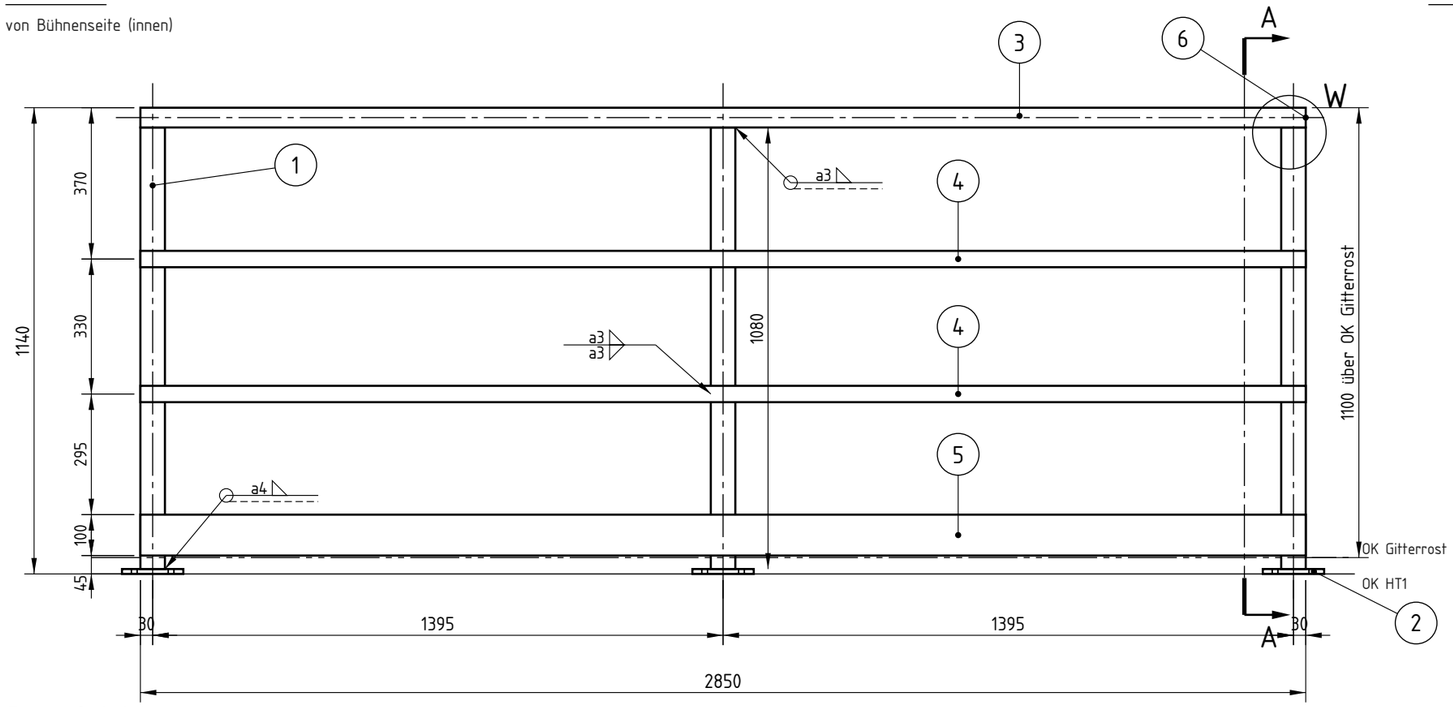


Schnitt A-A M 1:10

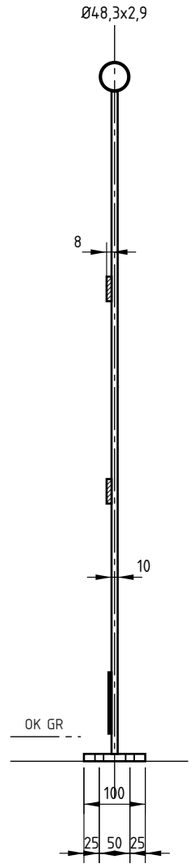


Detail W M 1:5

Handlaufende, Ronde Pos 6

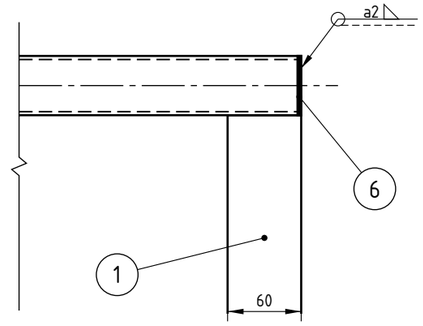

Draufsicht M 1:15

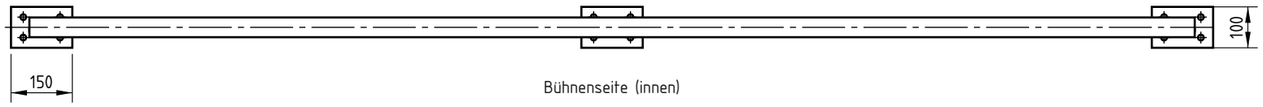

Bühnenseite (innen)

Hinweise


Anzahl: 4 Stück (2x Achse A, 2x Achse B), alle gleich.
Geländer nach DIN EN ISO 14122-3, OK Handlauf 1100 über OK Gitterrost, Horizontallast 0,5 kN/m.
Schweißnähte a3 umlaufend, soweit nicht angegeben.
Handlaufenden mit Ronden Pos 6 dicht verschweißt.
Befestigung je Pfosten 4x M12x40-8.8 auf HT1.

Stückliste GF1 (je Stück)

Pos	Stk	Benennung	Halbzeug	Werkstoff	Länge mm	Einzelgew. kg	Gesamtgew. kg
1	3	Pfosten	FL 60x10	S235JR	1080	5,09	15,27
2	3	Fußplatte	BL 12x100	S235JR	150	1,41	4,23
3	1	Handlauf	Rohr 48,3x2,9	S235JRH	2850	9,26	9,26
4	2	Knieleiste	FL 40x8	S235JR	2850	7,16	14,32
5	1	Fußleiste	FL 100x5	S235JR	2850	11,19	11,19
6	2	Abschlussronde	BL 3 Ø48	S235JR		0,043	0,090
		Gewicht je Baugruppe					**54,36**
		Gesamt 4 Stk					**217,44**

Detail Fußplatte M 1:5

Pos 2, BL 12, Lochbild = HT1 Obergurt

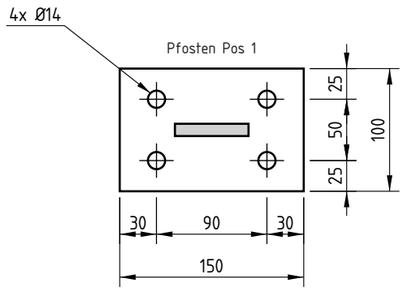

Index	Änderung	Datum	Name
-	Erstausgabe, Freigabe zur Fertigung	19.10.2026	T. Rehm

Werkstoff: S235JR / S235JRH	Oberfläche / Korrosionsschutz: gestrahlt Sa 2½, GB EP 80 µm, DB RAL 7016		Gewicht: **54,36 kg/Stk**
Allgemeintoleranzen: ISO 2768-mK	Schweißkonstruktionen: ISO 13920-BF	Ausführungsklasse: EXC2 (EN 1090-2)	Datum: 10/2026
Maßstab: 1:15 / 1:10 / 1:5	Format: A3 — Projektion	Auftrag: 26-115	Blatt: **5 / 5**

	Datum	Name
Bearb.	15.10.2026	M. Kranz
Gepr.	19.10.2026	T. Rehm
Freig.	19.10.2026	T. Rehm

Projekt: Erweiterung Lagerhalle 2
Kunde: Musterbau Projekt GmbH
Bauteil / Position: GF1, Achse A und B

Beispiel Metallbau GmbH
Stahl- und Metallbau
Industriestraße 12, 12345 Musterstadt

Schutzvermerk ISO 16016 beachten

Benennung: **Geländerfeld GF1**
Zusammenbau, L = 2850, 3 Pfosten, 4 Stück

Zeichnungsnummer: **BM-26-115-140**

Index: **-**