

Seitenansicht (von rechts) M 1:20

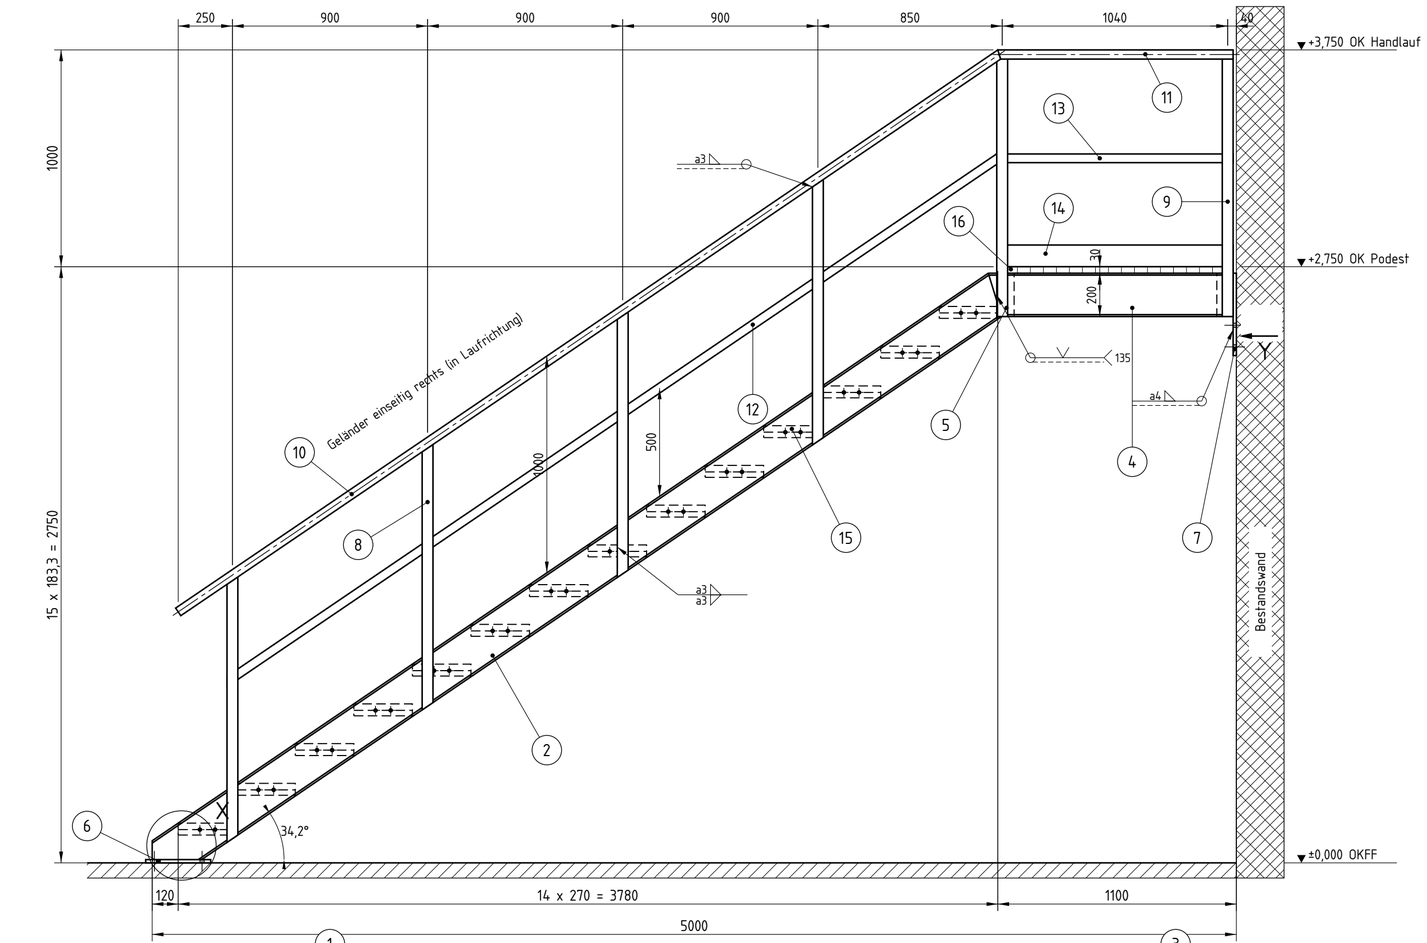


Draufsicht M 1:20

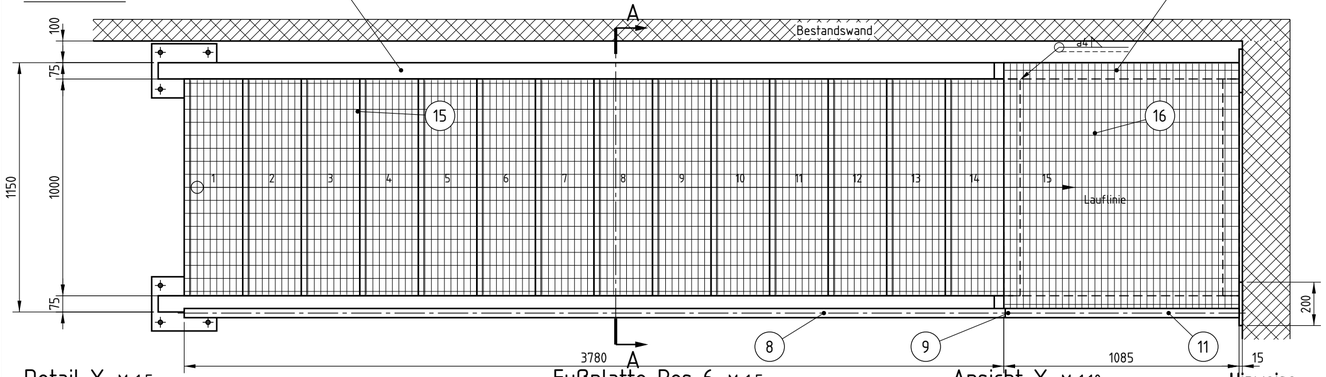


Schnitt A-A M 1:10

Wangen lotrecht geschnitten (UPN 200 bei 34,2°)

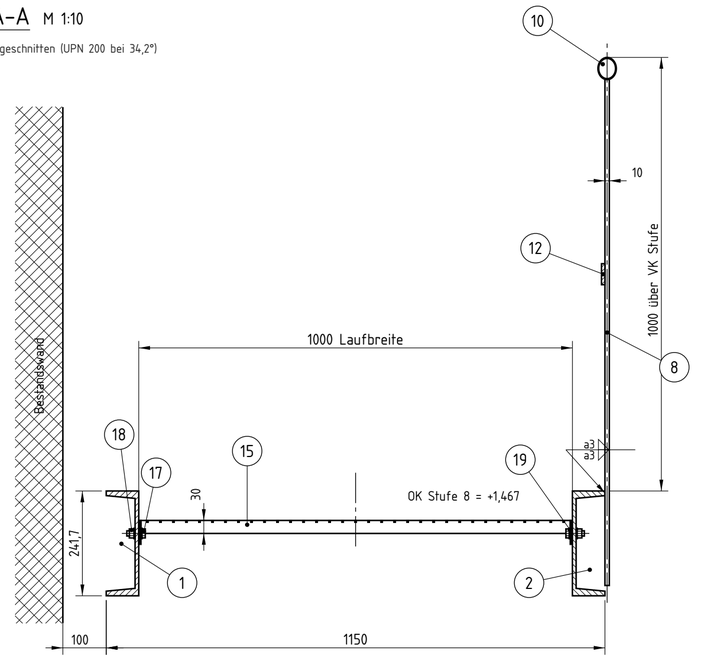


Detail X M 1:5

Fußpunkt Wange, je Seite

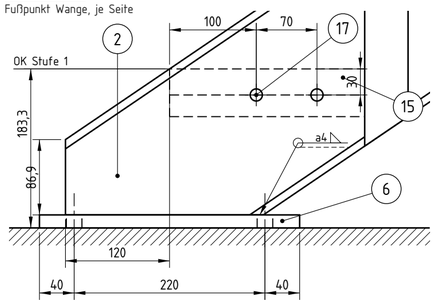


Fußplatte Pos 6 M 1:5

Draufsicht, Lage unter Wange rechts

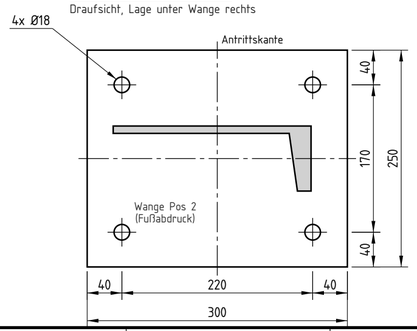

Ansicht Y M 1:10

Kopfplatte Pos 7 (rechts)

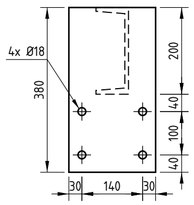

Stückliste

Pos	Stk	Benennung	Halbzeug / Profil	Werkstoff	Länge mm	Einzelgew. kg	Gesamtgew. kg
1	1	Wange links	UPN 200	S235JR	4661	117,92	117,92
2	1	Wange rechts (spiegelbildl. zu 1)	UPN 200	S235JR	4661	117,92	117,92
3	1	Podestwange links	UPN 200	S235JR	1129	28,56	28,56
4	1	Podestwange rechts (spiegelbildl.)	UPN 200	S235JR	1129	28,56	28,56
5	2	Podestquerträger	UPN 200	S235JR	1000	25,30	50,60
6	2	Fußplatte	BL 15x250	S235JR	300	8,83	17,66
7	2	Kopfplatte	BL 15x200	S235JR	380	8,95	17,90
8	4	Pfosten Lauf	FL 50x10	S235JR	1190	4,67	18,68
9	2	Pfosten Podest	FL 50x10	S235JR	1188	4,66	9,32
10	1	Handlauf Lauf	Rohr 42,4x2,6	S235JRH	4569	11,65	11,65
11	1	Handlauf Podest	Rohr 42,4x2,6	S235JRH	1085	2,77	2,77
12	1	Knieleiste Lauf	FL 40x8	S235JR	4297	10,79	10,79
13	1	Knieleiste Podest	FL 40x8	S235JR	1085	2,73	2,73
14	1	Fußleiste Podest	FL 100x5	S235JR	1085	4,26	4,26
15	14	Gitterroststufe m. Stufenwinkeln	1000x270 MW 30/30 TS 30x3	Kaufteil, fvz	1000	12,60	176,40
16	1	Gitterrost Podest	1085x1150 MW 30/30 TS 30x3	Kaufteil, fvz	1150	40,18	40,18
17	56	Sechskantschraube	ISO 4017 M12x35	8.8 fvz	35	0,047	2,63
18	56	Sechskantmutter	ISO 4032 M12	8 fvz		0,017	0,95
19	112	Scheibe	ISO 7089 12	200 HV fvz		0,006	0,67
		Gesamtgewicht					**660,15**

Hinweise

1. Ausführung nach DIN EN 1090-2, EXC2. Alle Maße in mm.
2. Schweißnähte a3 umlaufend, soweit nicht anders angegeben. Schweißverfahren 135 (MAG). Bewertungsgruppe C nach ISO 5817.
3. Alle Kanten gebrochen, Schnittkanten entgratet.
4. Zinkentlüftungsbohrungen Ø10 an allen geschlossenen Querschnitten vorsehen (Rohre, Gehrungen).
5. Gitterroststufen nach DIN 24531-1, Gitterrost nach DIN 24537-1, Rutschhemmung R11, feuerverzinkt.
6. Stufenbefestigung: je Stufe und Wange 2x Ø14 (56 Bohrungen), Lochabstand 70, 30 unter OK Stufe, siehe Detail X.
7. Verankerung Fuß- und Kopfplatten bauseits nach Statik (Schwerlastanker M16, nicht im Lieferumfang).
8. Steigungsverhältnis 15 x 183,3 / 270 nach DIN 18065.

Index	Änderung	Datum	Name
a	Handlauf Podest bis Wand geführt, Pos 11 geändert	21.10.2026	M. Kranz
-	Erstausgabe, Freigabe zur Fertigung	16.10.2026	T. Rehm

Werkstoff: S235JR / S235JRH	Oberfläche / Korrosionsschutz: feuerverzinkt DIN EN ISO 1461 (tZn)		Gewicht: **660,15 kg**
Allgemeintoleranzen: ISO 2768-mK	Schweißkonstruktionen: ISO 13920-BF	Ausführungsklasse: EXC2 (EN 1090-2)	Datum: 10/2026
Maßstab: 1:20 / 1:10 / 1:5	Format: A2 — Projektion:	Auftrag: 26-114	Blatt: 1 / 1

	Datum	Name
Bearb.	14.10.2026	M. Kranz
Gepr.	16.10.2026	T. Rehm
Freig.	16.10.2026	T. Rehm

Projekt: Erweiterung Lagerhalle 2
Kunde: Musterbau Projekt GmbH
Bauteil / Position: Treppe ST-01, Achse 4 / C-D

Beispiel Metallbau GmbH
Stahl- und Metallbau
Industriestraße 12, 12345 Musterstadt

Schutzvermerk ISO 16016 beachten

Benennung: **Stahltreppe mit Podest**
Zusammenbau ST-01, 15 Stg. 183,3/270, Laufbreite 1000

Zeichnungsnummer: **BM-26-114-100**
Index: **a**